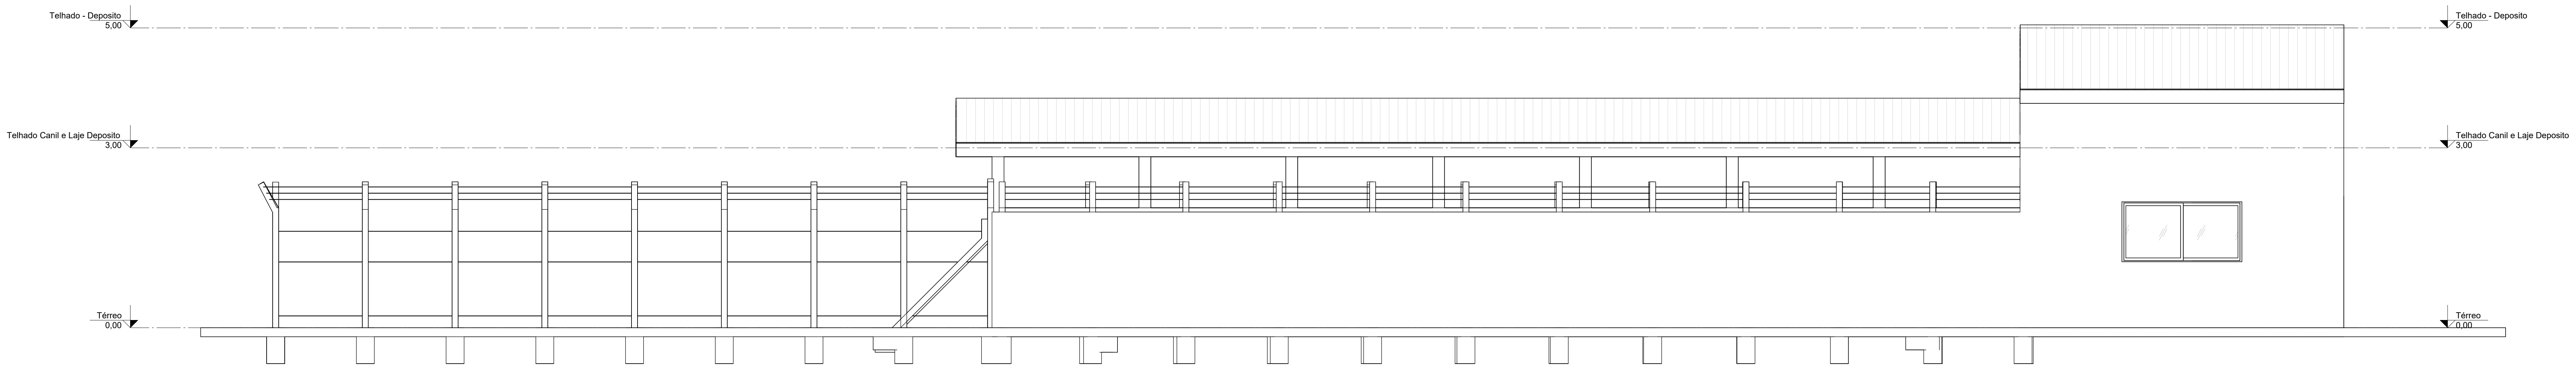

5 **FACHADA FRONTAL**
escala 1 : 50

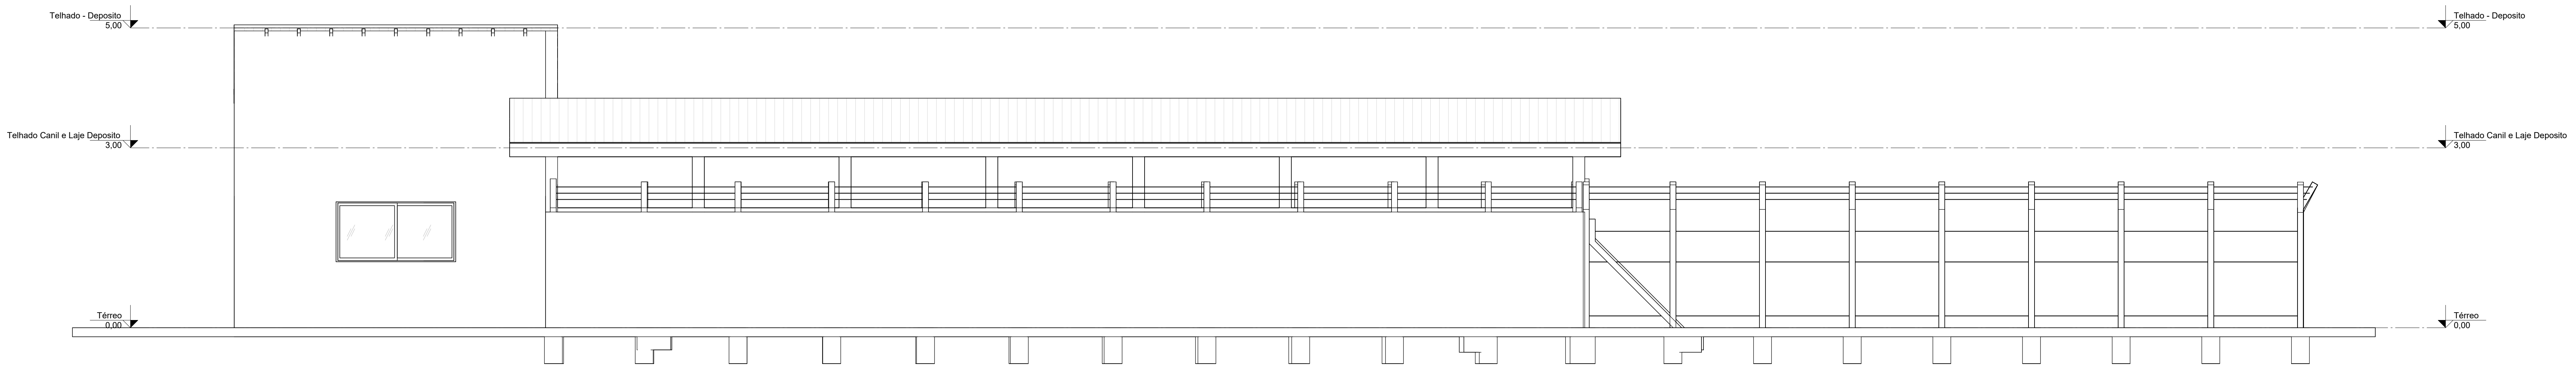

6 **FACHADA FUNDOS**
escala 1 : 50

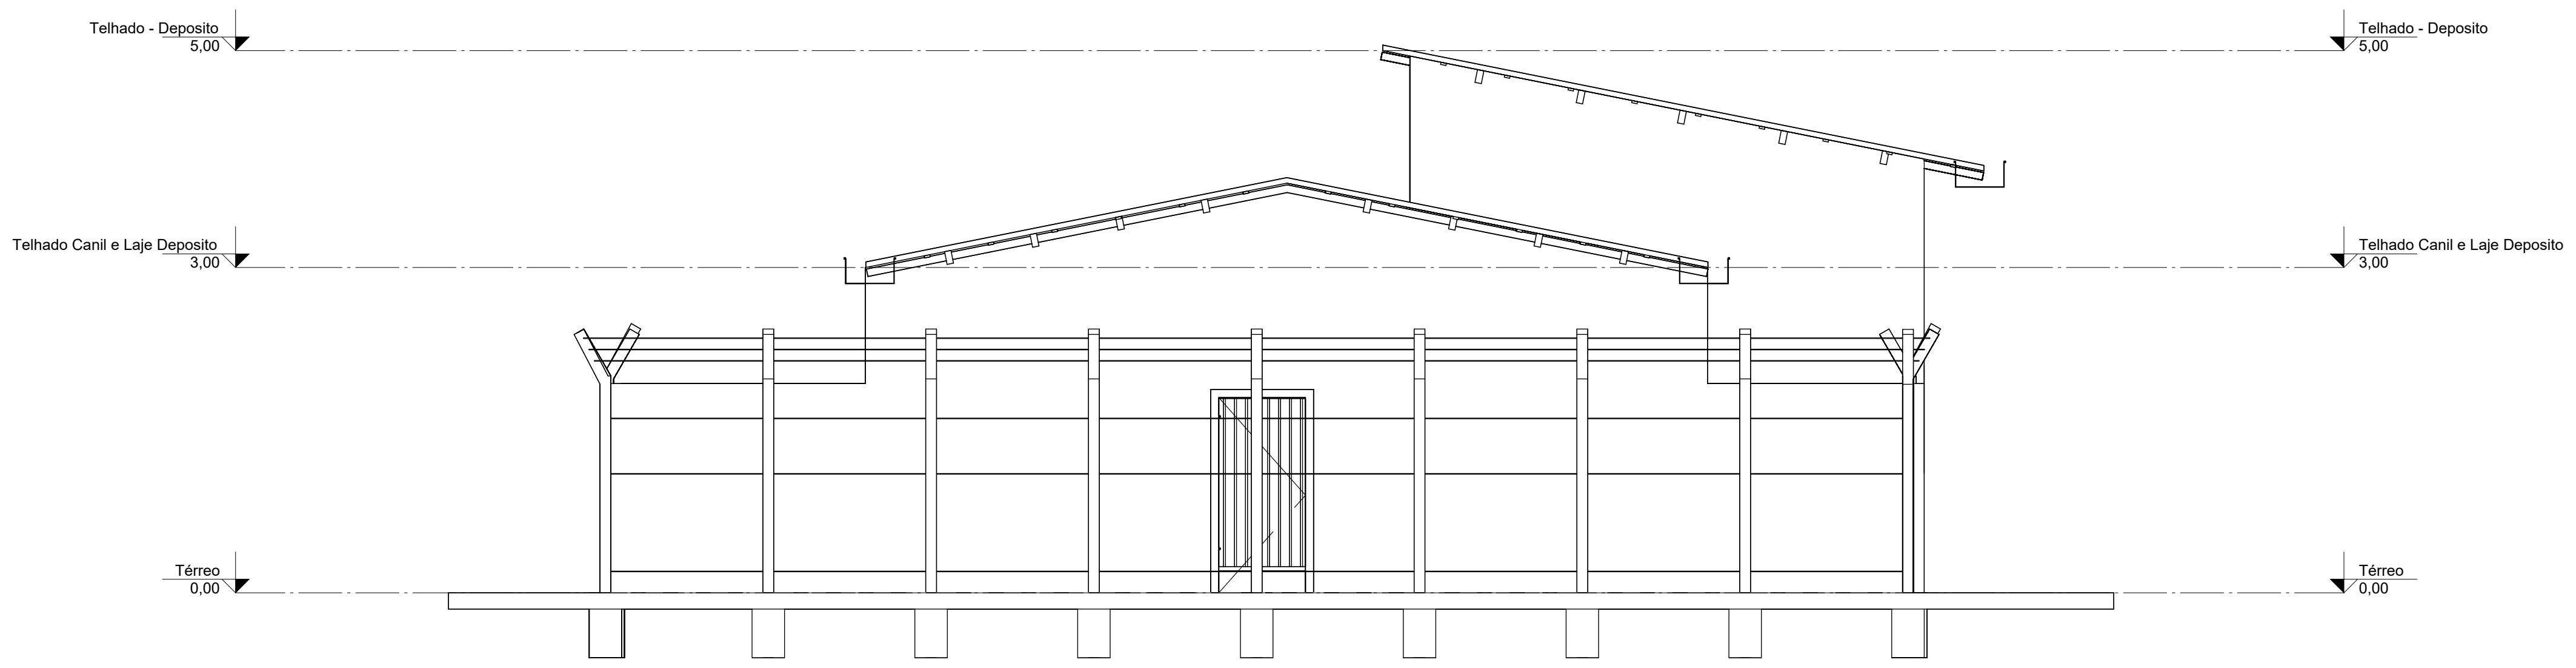

7 **FACHADA ESQUERDA**
escala 1 : 50

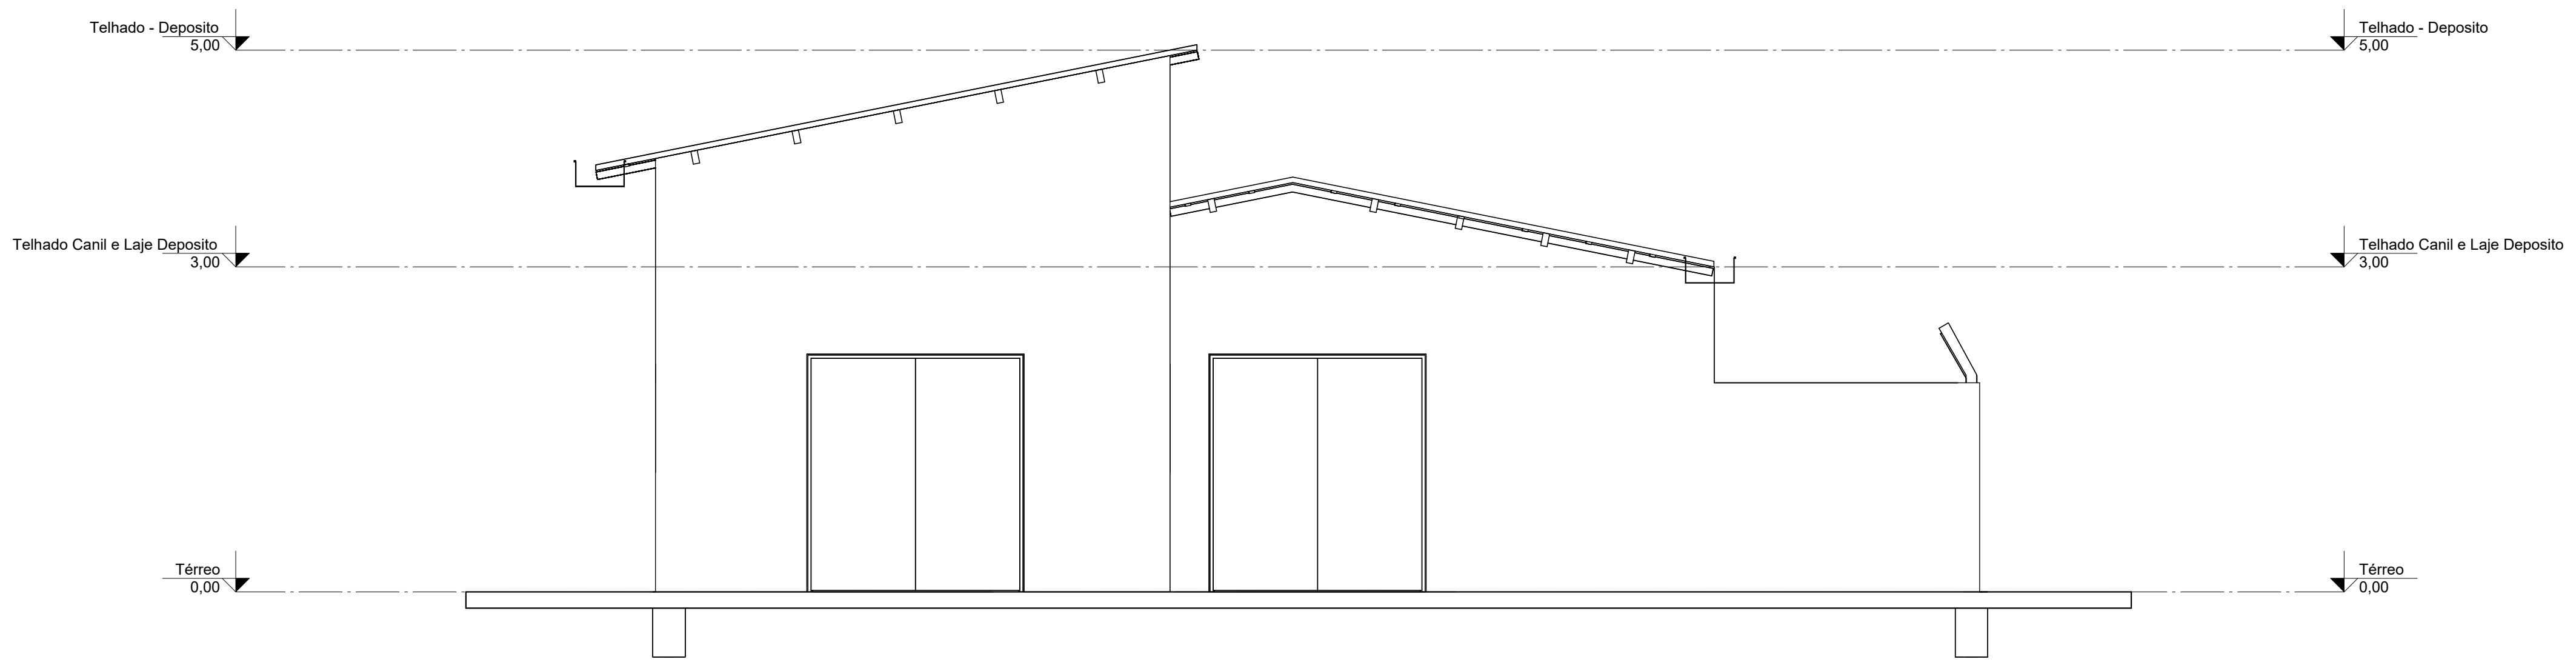

8 **FACHADA DIREITA**
escala 1 : 50

MD EB DEC DOM IME	ANO 2026	Nº OPUS 00	ITEM AR	FOLHA 01/03
OM IME		LOCAL MARAMBAIA - BELÉM		
OBRA CONSTRUÇÃO DO CANIL DA 15º CIA PE				DATA 11/11/2026
PRANCHA FACHADAS				DIM METRO
AUTOR CAP FELIPE MIRANDA		VISTO AUTOR		DESENHISTA Autor
CH SEC TEC		VISTO CH SEC TEC		ESCALA INDICADA
CH CRO 5		VISTO CH CRO		ARQUIVO arquivo.rvt

Rua 31 De Março,3018 – Pinheirinho, Curitiba–PR
Cep: 81150–280 – Fone:(41) 3268–0147