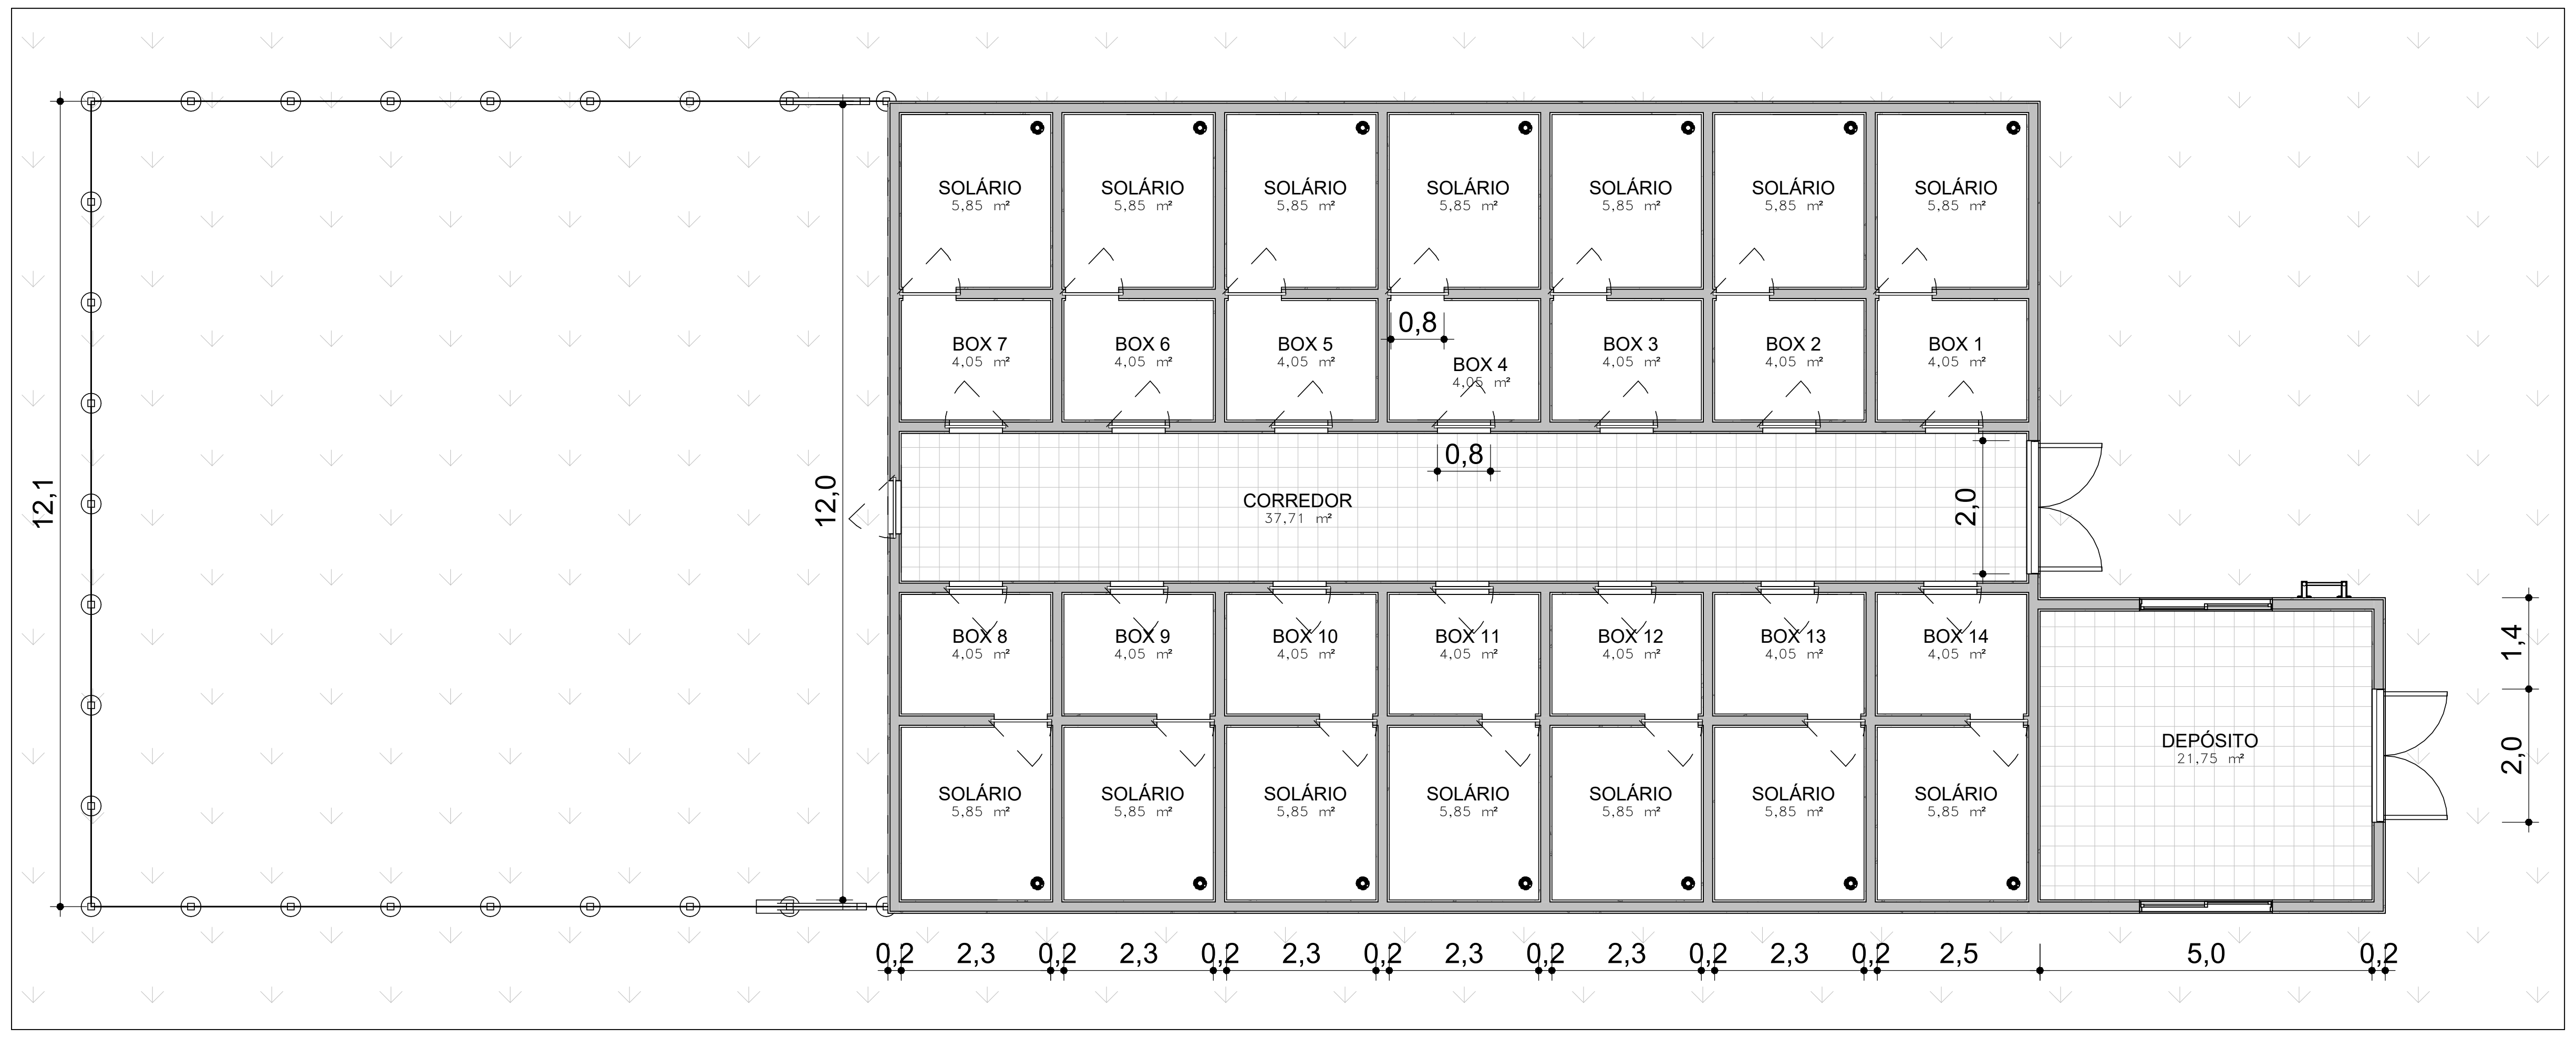

1 **PLANTA TÉRREO**
escala 1 : 100

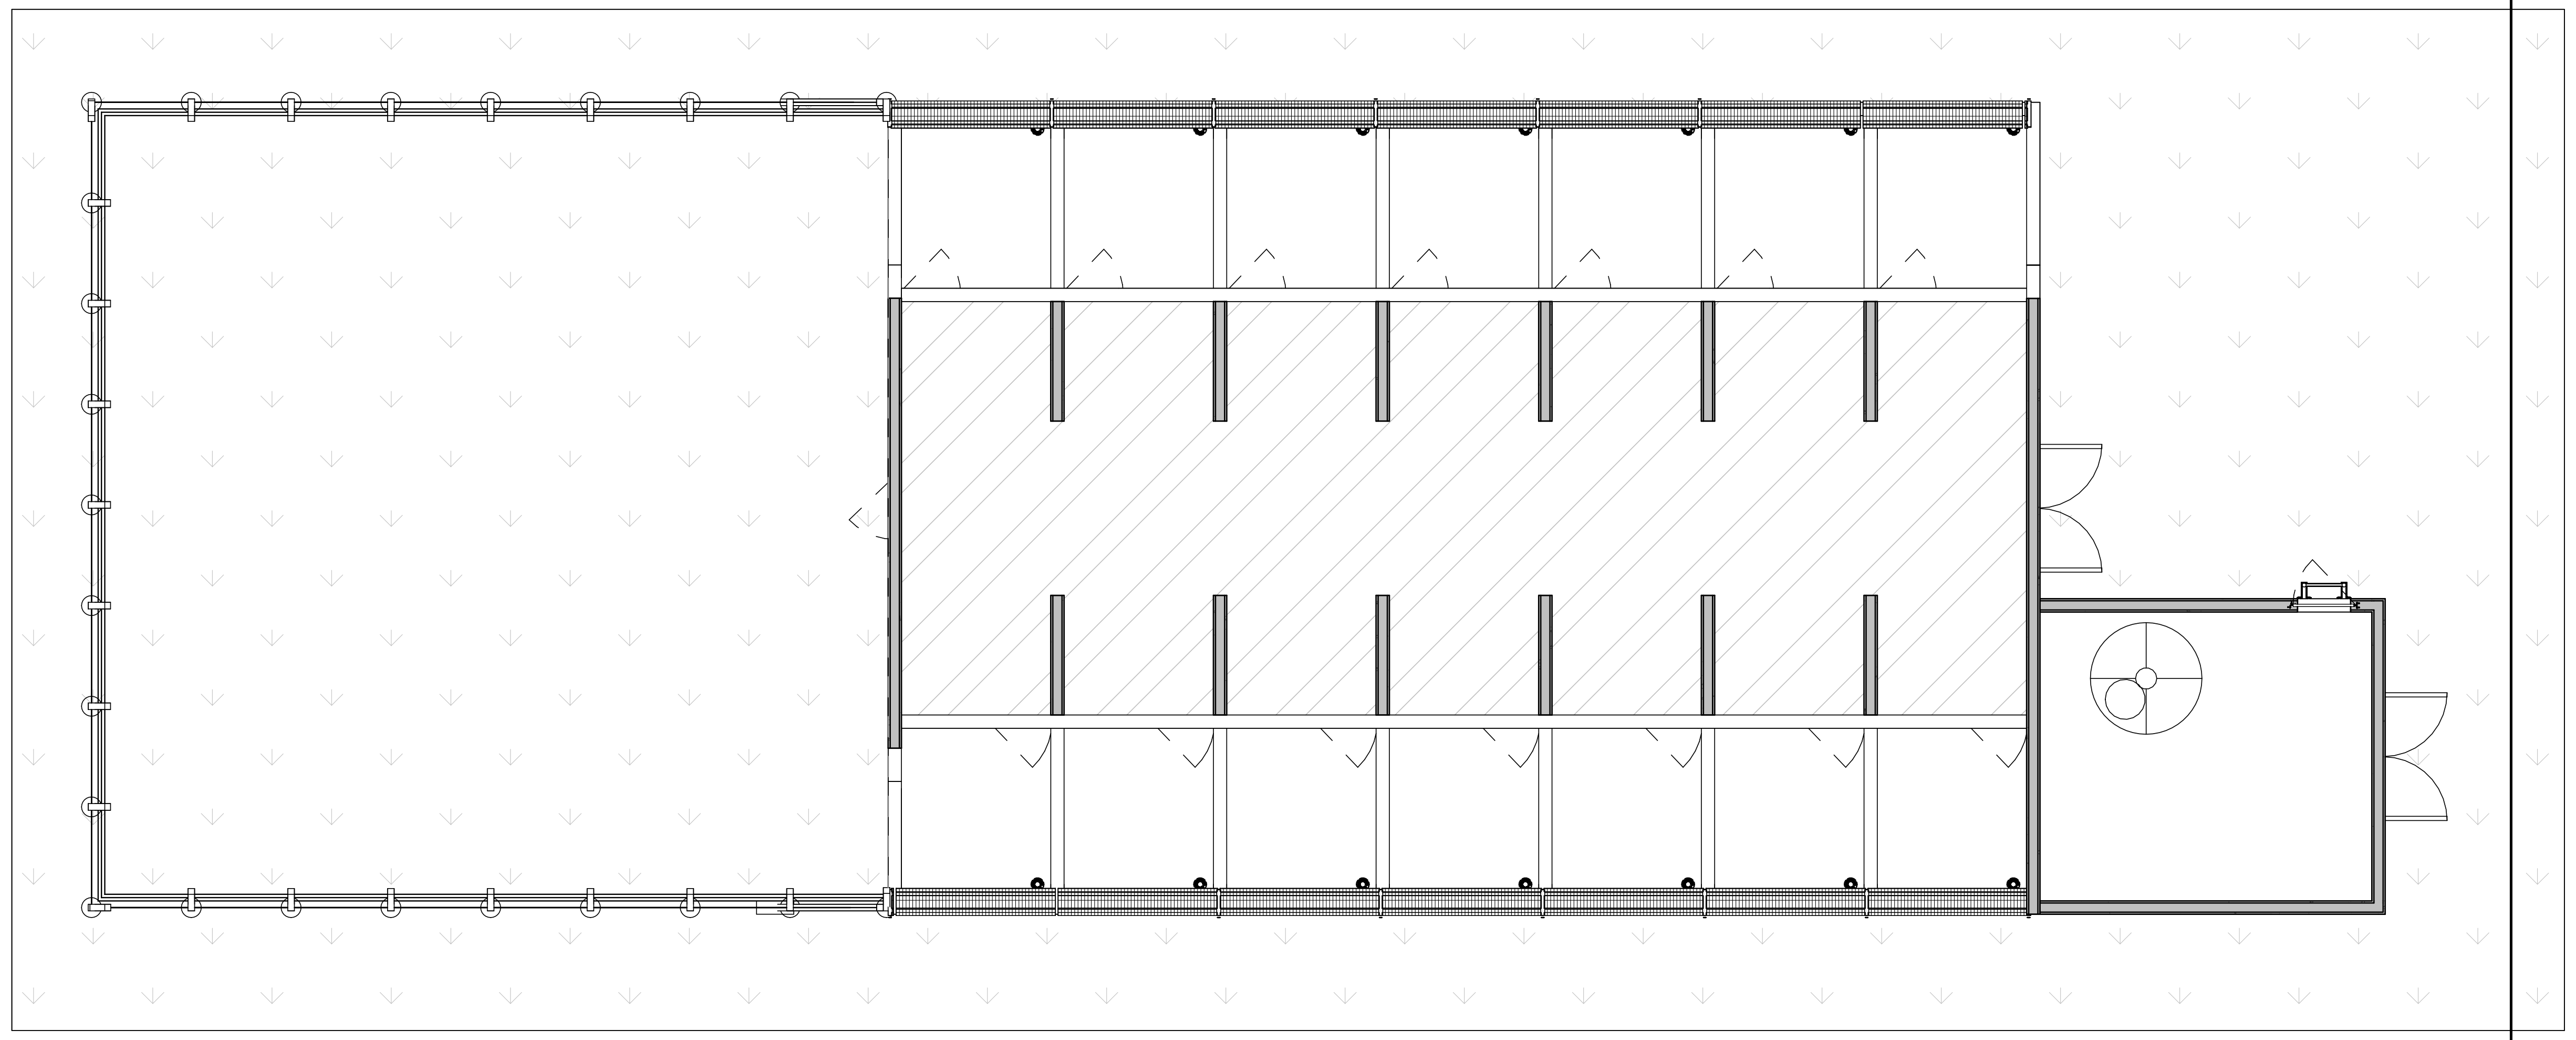

3 **PLANTA LAJE**
escala 1 : 100

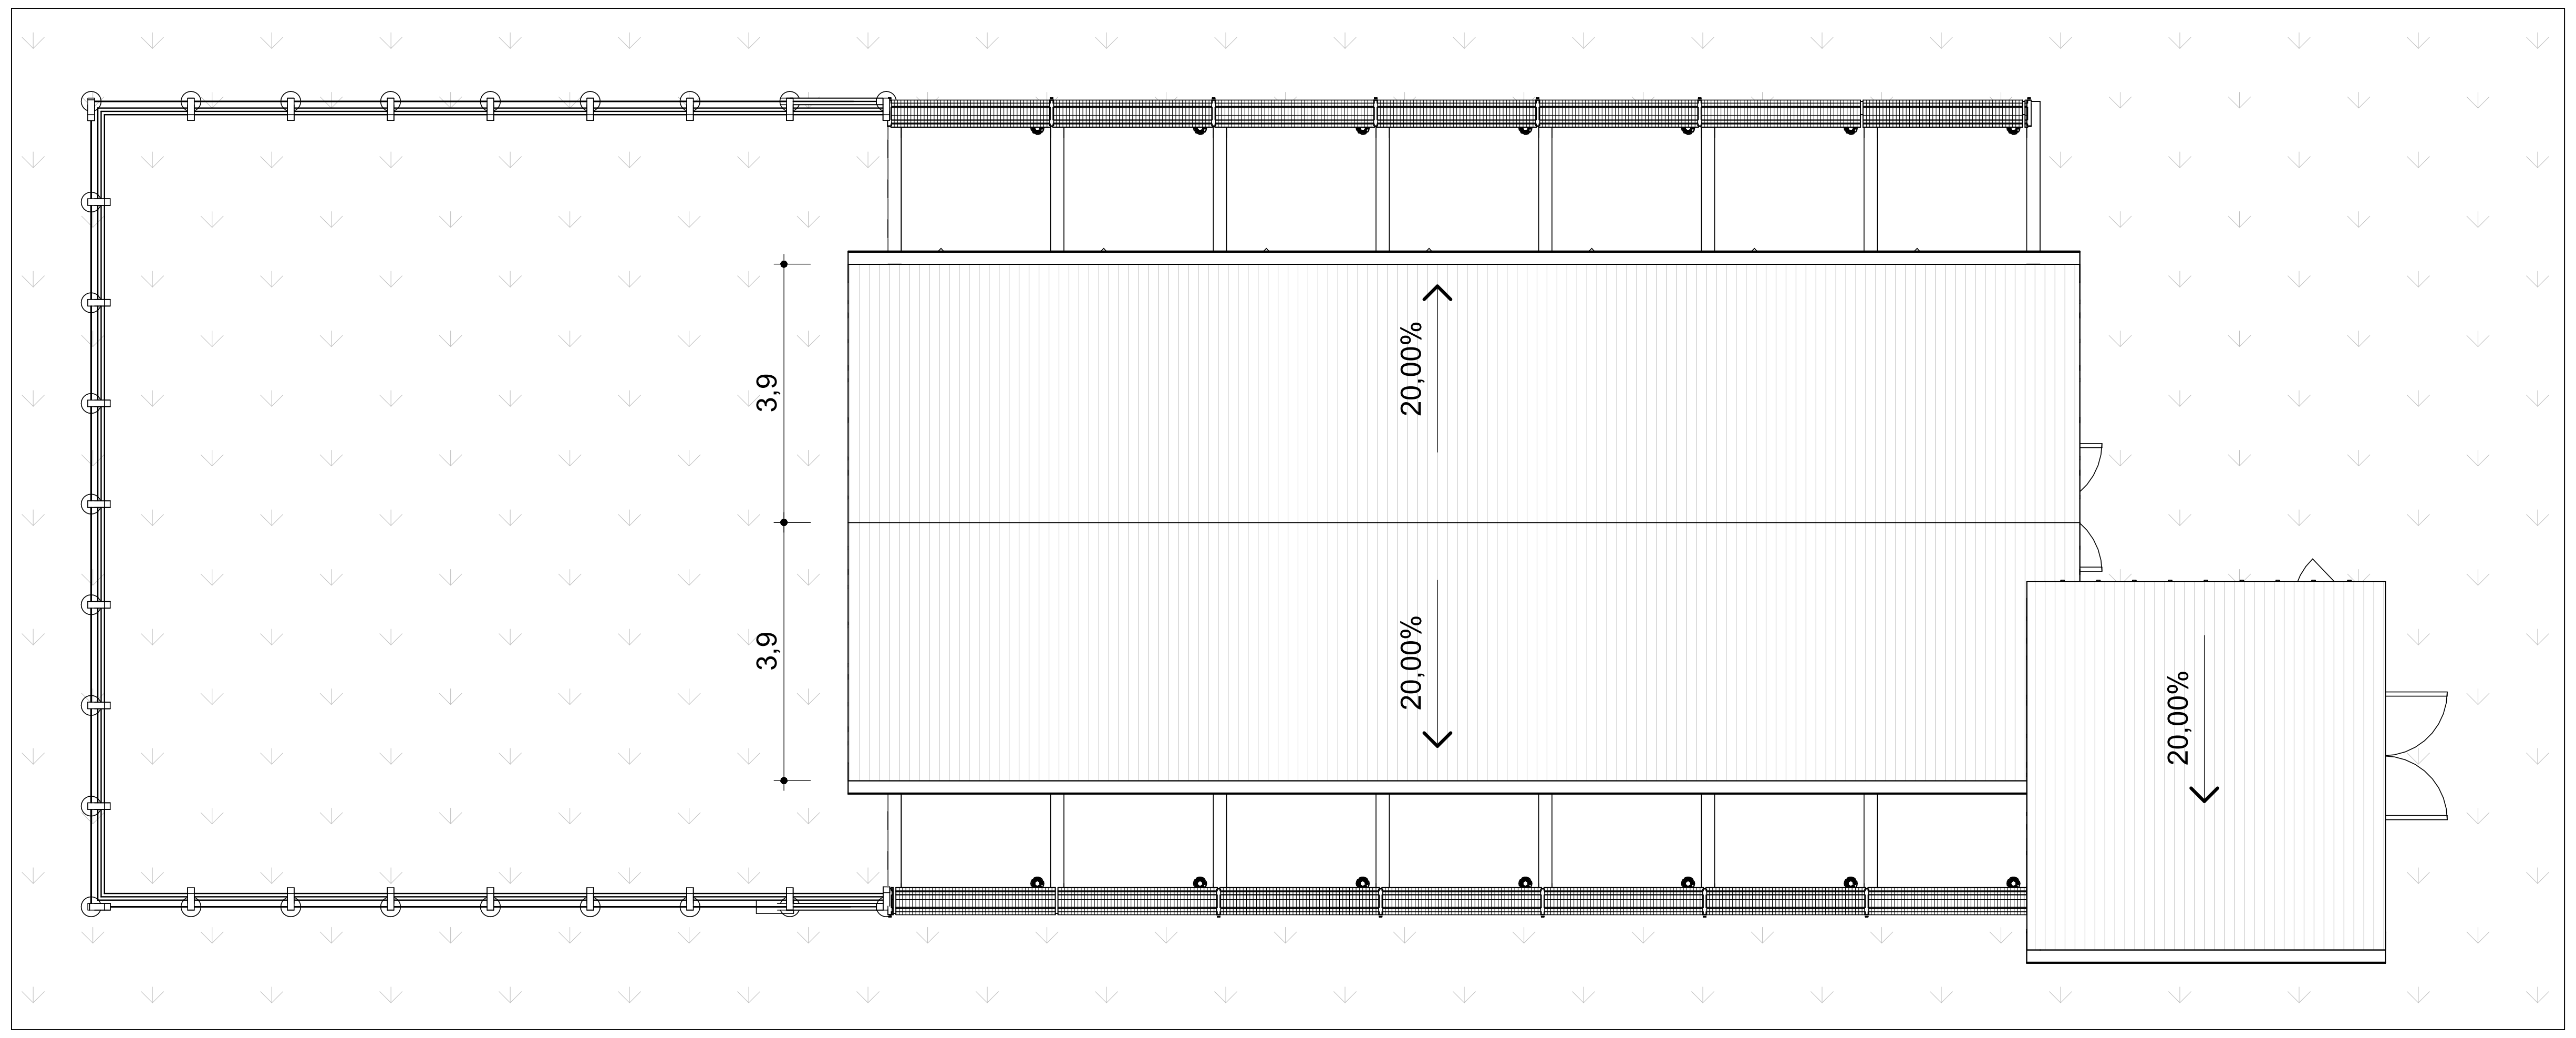

2 **PLANTA TELHADO**
escala 1 : 100

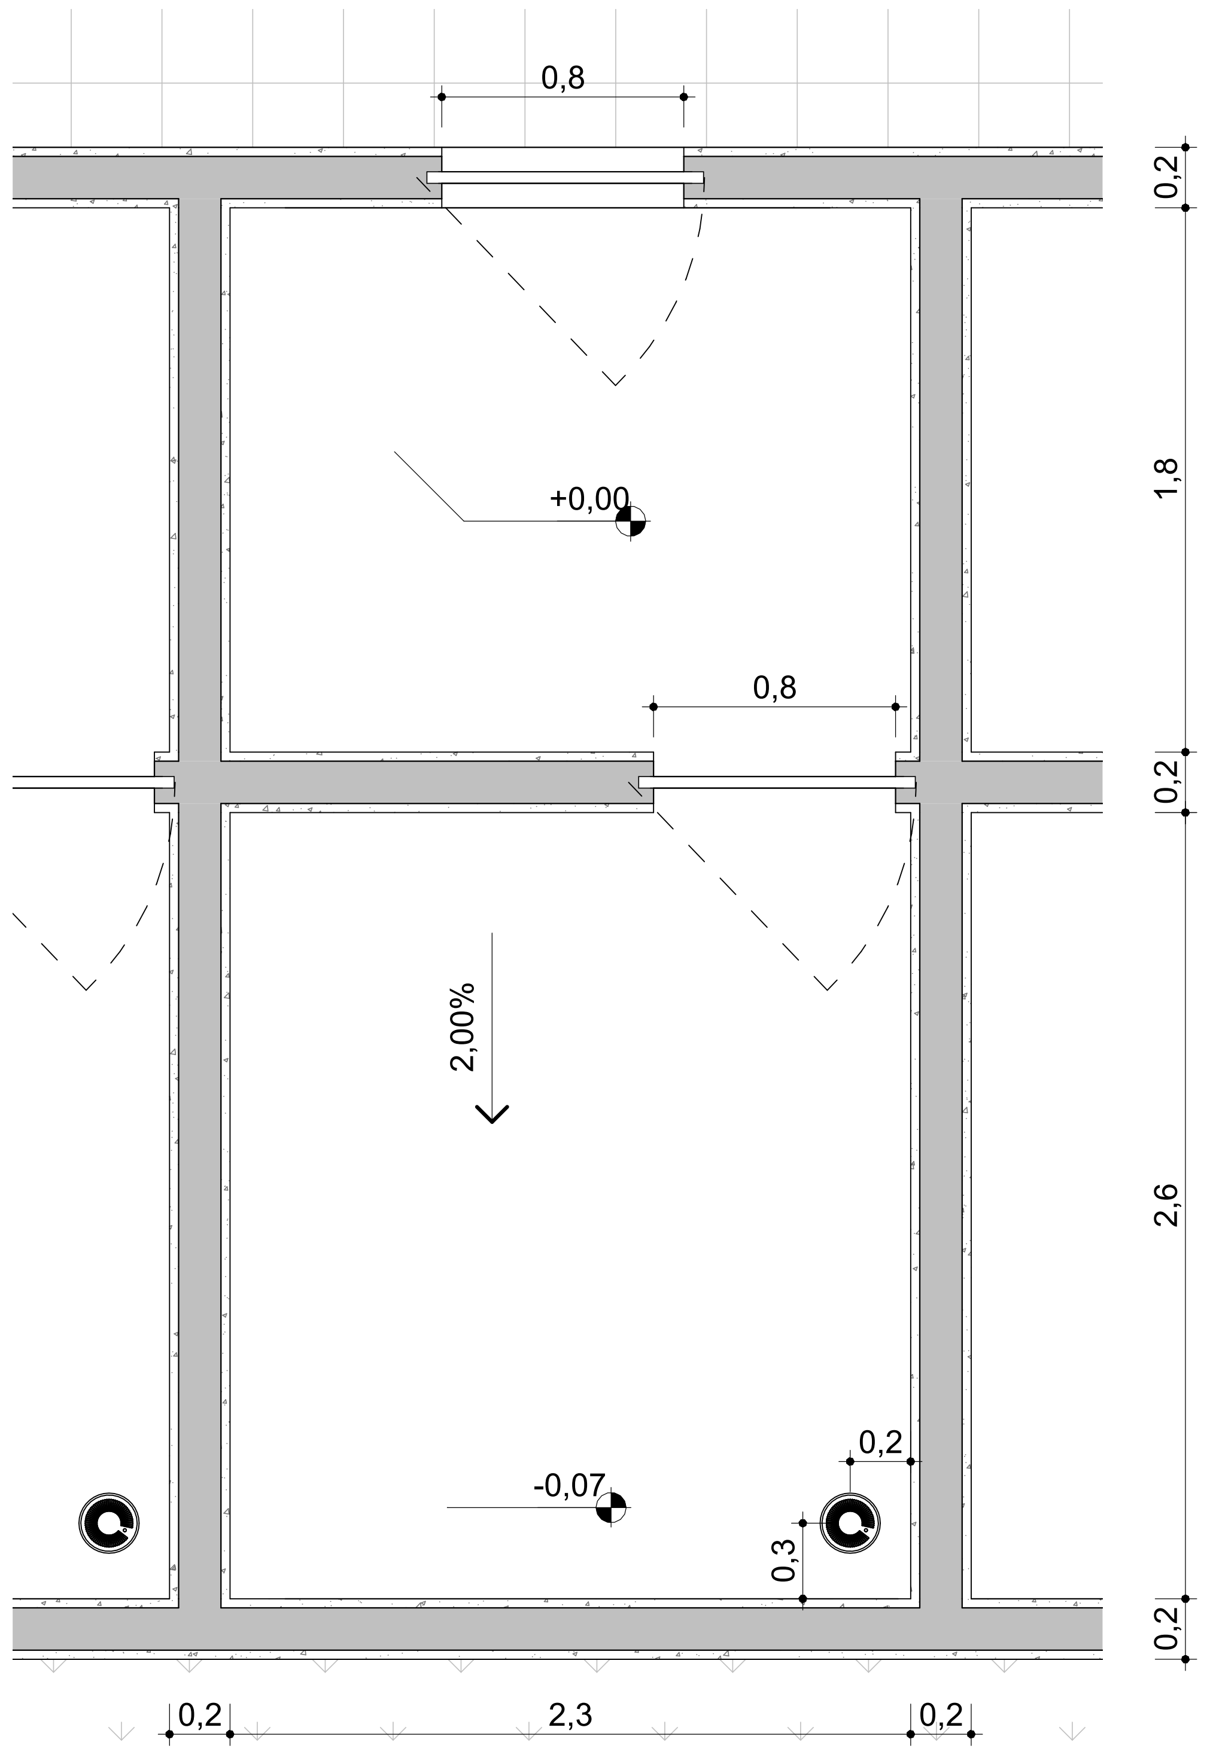

4 **PLANTA BAIXA BOX TIPO**
escala 1 : 25

A - TABELA JANELAS

FAMÍLIA E TIPO	LARGURA	ALTURA	PEITORIL	QUANT.
CORRER - 2 FOLHAS	2,0	1,0	1,1	2

B - TABELA DE PORTAS

FAMÍLIA E TIPO	LARGURA	ALTURA	QUANT.
	0,8	2,1	1
PORTA DE ABRIR 02 FOLHAS COM VISOR	2,0	2,2	2
PORTÃO METÁLICO | GRADIL	0,8	1,2	1
PORTÃO METÁLICO | GRADIL	0,8	1,8	28

C - TABELA DE PISOS

FAMÍLIA E TIPO	ÁREA
Piso: NormaDOM - Osso - 15cm - Laje Concreto	21,75 m²
Piso: NormaDOM - Revestimento - 5cm - Piso Cerâmica 45x45cm	118,93 m²
Piso: NormaDOM - Revestimento - 5cm - Piso Concreto	244,63 m²

D - TABELA DE PAREDES

FAMÍLIA E TIPO	COMPRIMENTO	ÁREA
Parede básica: CRO5 - Alvenaria - 20cm - Tijolo Cerâmico	199,5 m	428,25 m²

E - TABELA DE TETOS

FAMÍLIA E TIPO	ÁREA
CRO5 - Telha Fibrocimento Ondulada	175,40 m²

G - ALAMBRADO

FAMÍLIA E TIPO	COMPRIMENTO
Guarda-corpo: Alambrado	36,2 m

H - DIVERSOS

FAMÍLIA E TIPO	QUANT.	COMPRIMENTO
CAIXA D'ÁGUA 2000 L	1	0,0
ESCADA DE MARINHEIRO	1	0,0
PAINEL DE GRADIL	2	34,3
RALO CIRCULAR	14	0,0

F - TABELA DE ÁREA TOTAL ÚTIL

LOCAL	ÁREA
BOX 1	4,05 m²
BOX 2	4,05 m²
BOX 3	4,05 m²
BOX 4	4,05 m²
BOX 5	4,05 m²
BOX 6	4,05 m²
BOX 7	4,05 m²
BOX 8	4,05 m²
BOX 9	4,05 m²
BOX 10	4,05 m²
BOX 11	4,05 m²
BOX 12	4,05 m²
BOX 13	4,05 m²
BOX 14	4,05 m²
CORREDOR	37,71 m²
DEPÓSITO	21,75 m²
SOLÁRIO	81,90 m²
	198,06 m²

E - TABELA DE FORRO

Família e tipo	ÁREA
Forro composto: NormaDOM - 1.5cm - Forro Metálico	105,51 m²
Forro composto: NormaDOM - 1.5cm - Forro Metálico	21,75 m²

QUADRO DE MODIFICAÇÕES

L	DATA	DESCRIÇÃO	RESP	VISTO
A				
B				
C				
D				
E				

OBSERVAÇÕES

MD EB DEC DOM IME	ANO 2026	Nº OPUS 00	ITEM AR	FOLHA 02/03

OM IME
LOCAL MARAMBAIA - BELÉM

OBRA CONSTRUÇÃO DO CANIL DA 15º CIA PE
PRANCHA CONSOLIDACAO - PLANTA GERAL E QUANTITATIVOS
DATA 11/11/26
DIM METRO

AUTOR CAP FELIPE MIRANDA
VISTO AUTOR
DESENHISTA Autor
CH SEC TEC
VISTO CH SEC TEC
ESCALA INDICADA
CH CRO 5
VISTO CH CRO
ARQUIVO arquivo.rvt

Rua 31 De Março,3018 – Pinheirinho, Curitiba–PR
Cep: 81150–280 – Fone:(41) 3268–0147