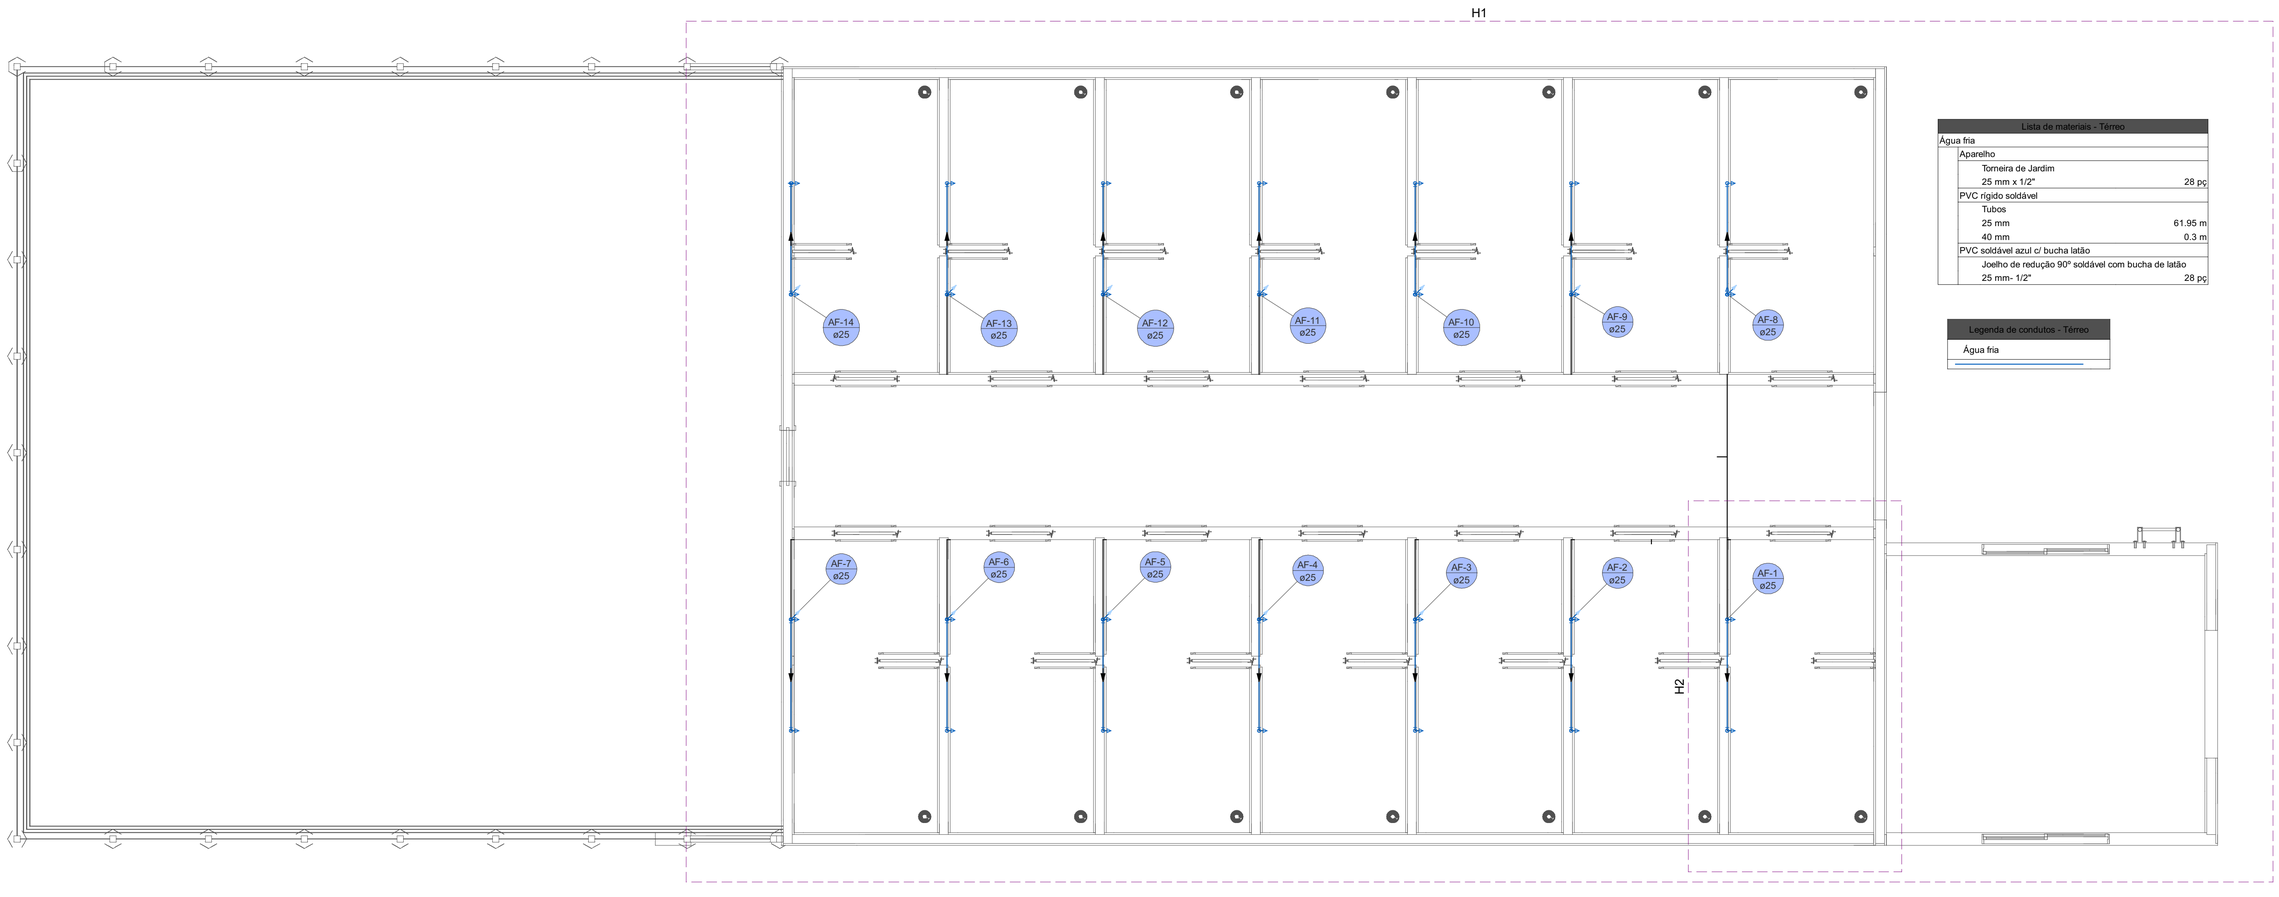


Lista de materiais - Térreo	
Água fria	
Aparelho	
Torneira de Jardim	
25 mm x 1/2"	28 pç
PVC rígido soldável	
Tubos	
25 mm	61.95 m
40 mm	0.3 m
PVC soldável azul c/ bucha latão	
Joelho de redução 90° soldável com bucha de latão	
25 mm- 1/2"	28 pç

Legenda de condutos - Térreo
Água fria

1:50