
Lista de materiais - Térreo		
Água fria		
	Aparelho	
	Torneira de Jardim	
	25 mm x 1/2"	2 pç
	PVC rígido soldável	
	Tubos	
	25 mm	4.45 m
	PVC soldável azul c/ bucha latão	
	Joelho de redução 90º soldável com bucha de latão	
	25 mm- 1/2"	2 pç

Legenda de condutos - Térreo
Água fria

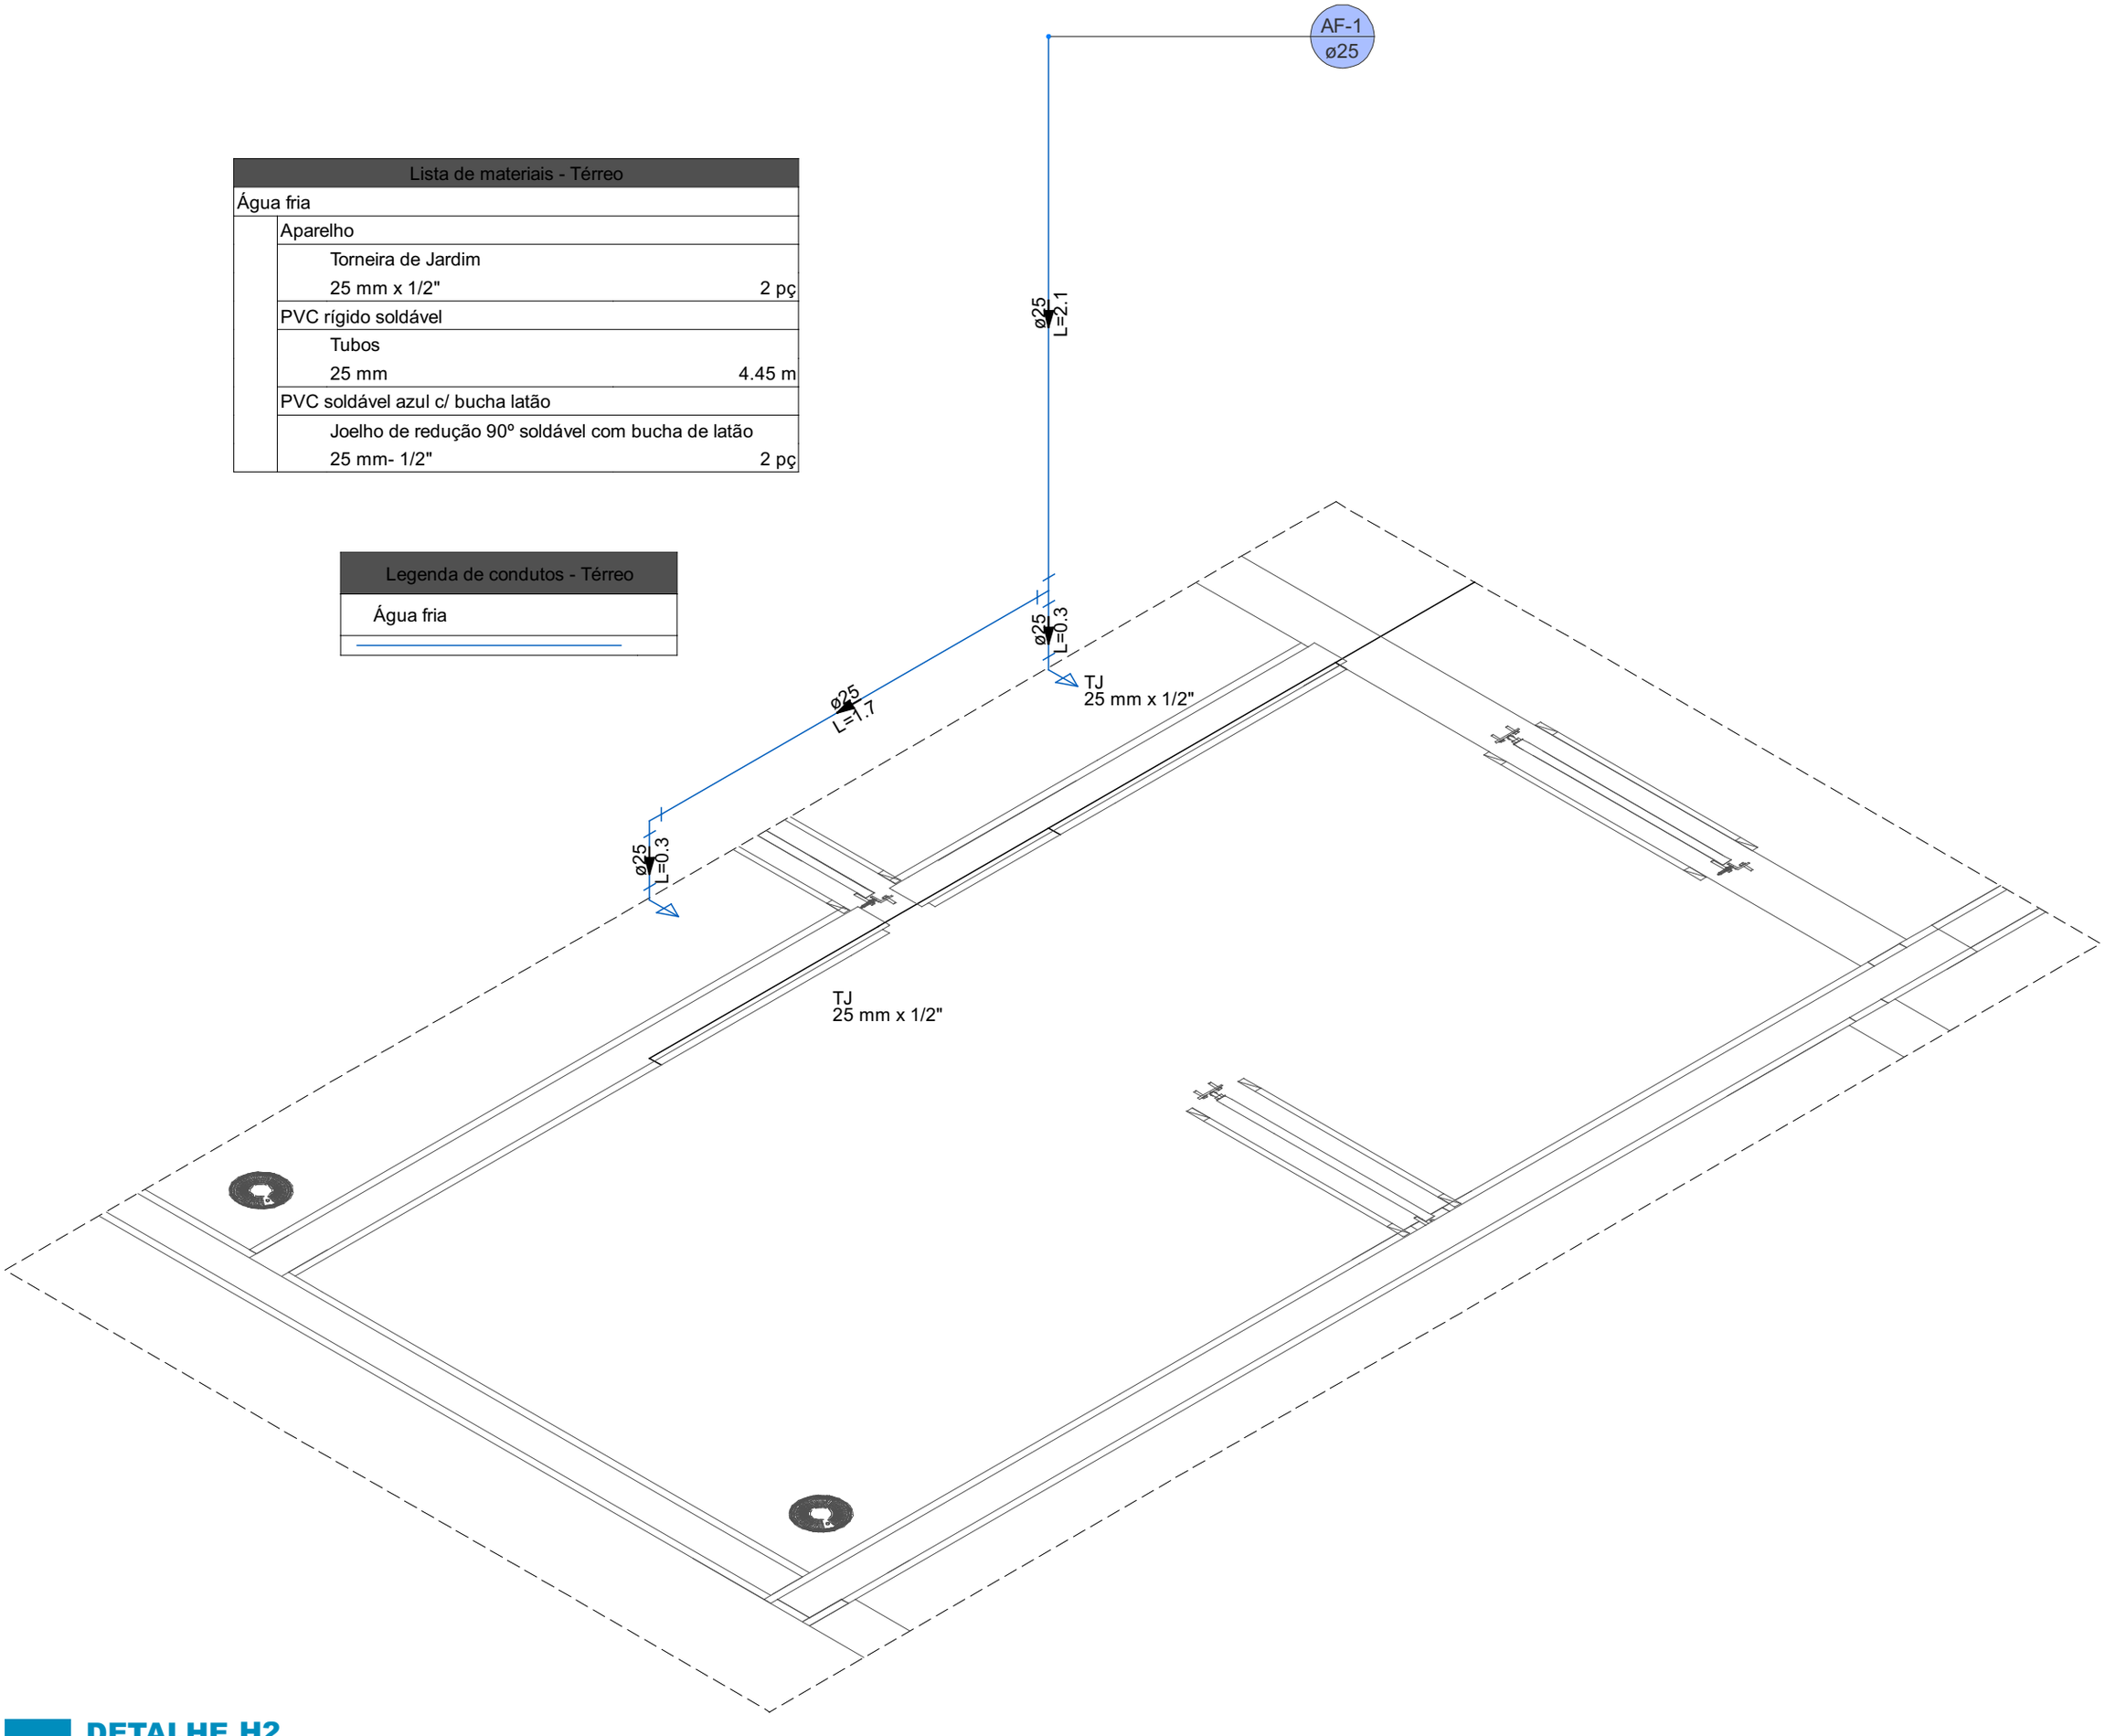

DETALHE H2

1:25