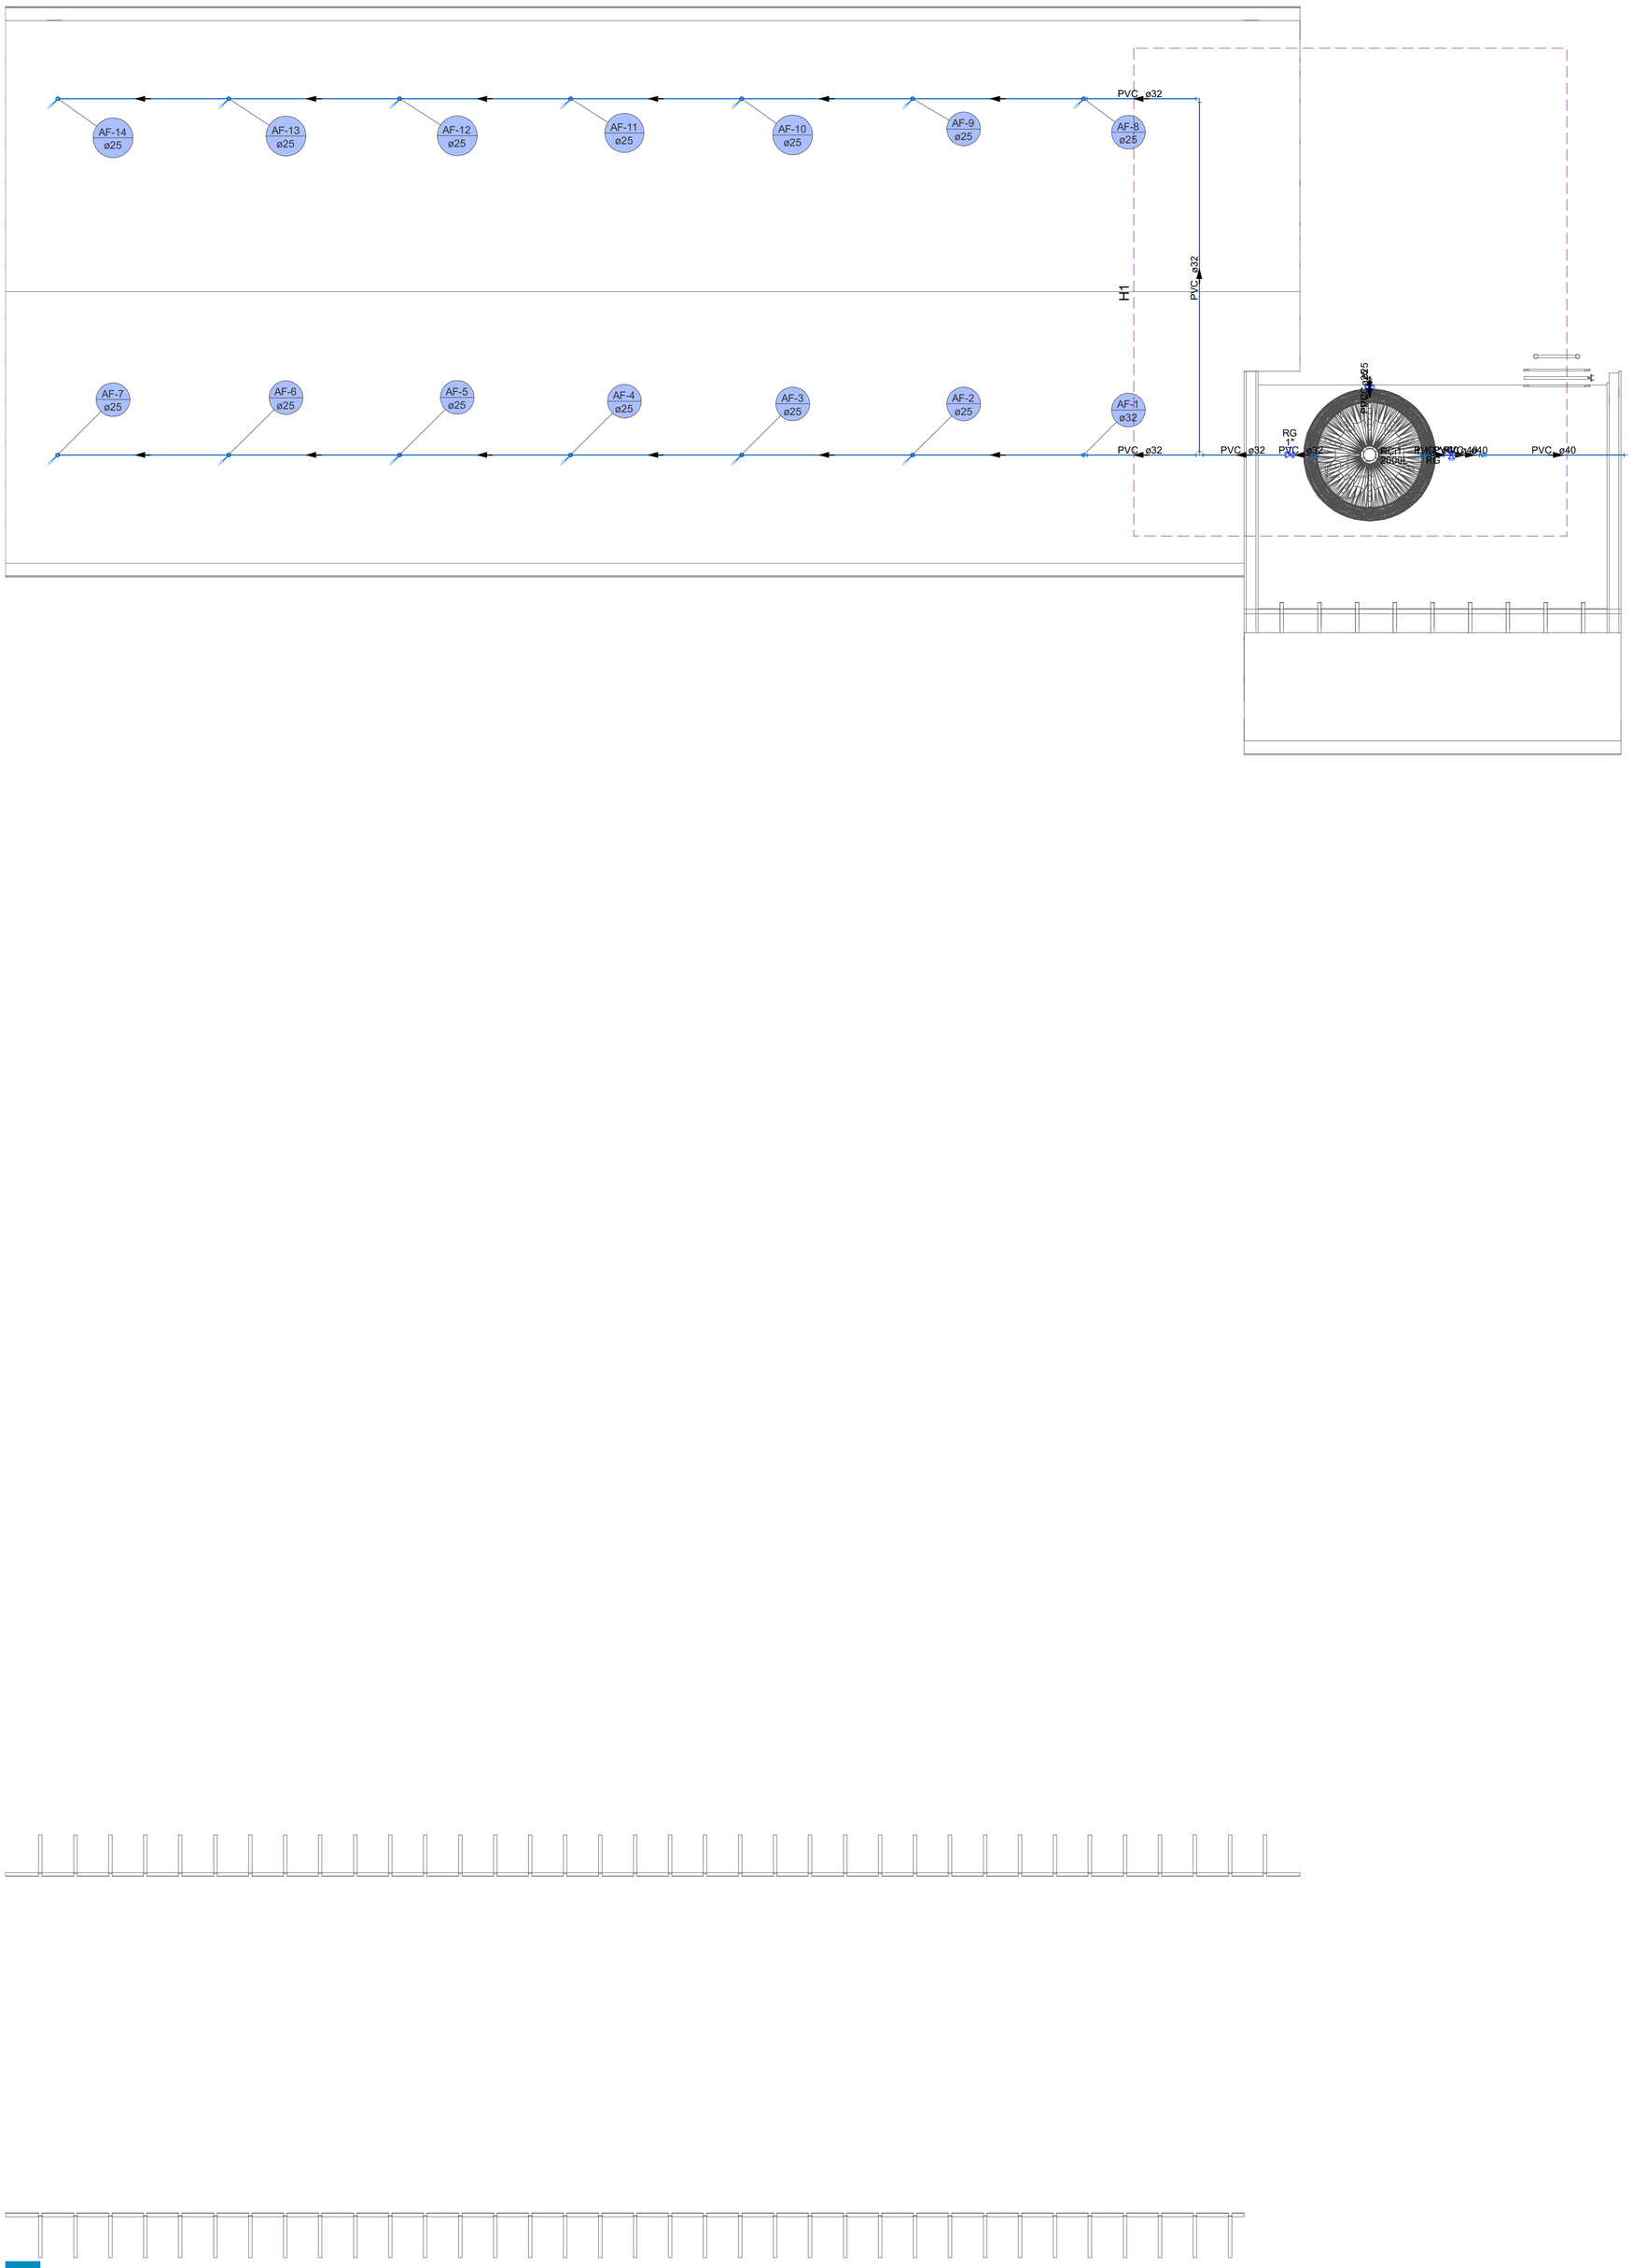


Lista de materiais - Telhado Canil e Laje Deposito		
Alimentação		
	Metais	
	Registro bruto de gaveta industrial 3/4"	1 pç
	PVC rígido soldável	
	Adapt sold c/ flange fixo p cx. d´água 25 mm - 3/4"	1 pç
	Adapt sold.curto c/bolsa-rosca p registro 25 mm - 3/4"	2 pç
	Joelho 90° soldável 25 mm	1 pç
	Tubos 25 mm	0.85 m
Água fria		
	Metais	
	Registro bruto de gaveta industrial 1"	1 pç
	Registro de gaveta bruto ABNT 1.1/4"	1 pç
	PVC rígido soldável	
	Adapt sold c/ flange fixo p cx. d´água 40 mm - 1.1/4"	2 pç
	Adapt sold.curto c/bolsa-rosca p registro 32 mm - 1"	2 pç
	40 mm - 1.1/4"	2 pç
	Curva 90 soldável 32 mm	2 pç
	Joelho 90° soldável 32 mm	2 pç
	40 mm	1 pç
	Tubos 25 mm	0.26 m
	32 mm	39.22 m
	40 mm	4.22 m
	Tê 90 soldável 32 mm	2 pç
	40 mm	1 pç
	Reservatório cilíndrico	
	Polietileno 2000 L	1 pç

Legenda de condutos - Telhado Canil e Laje Deposito
Água fria
Alimentação