

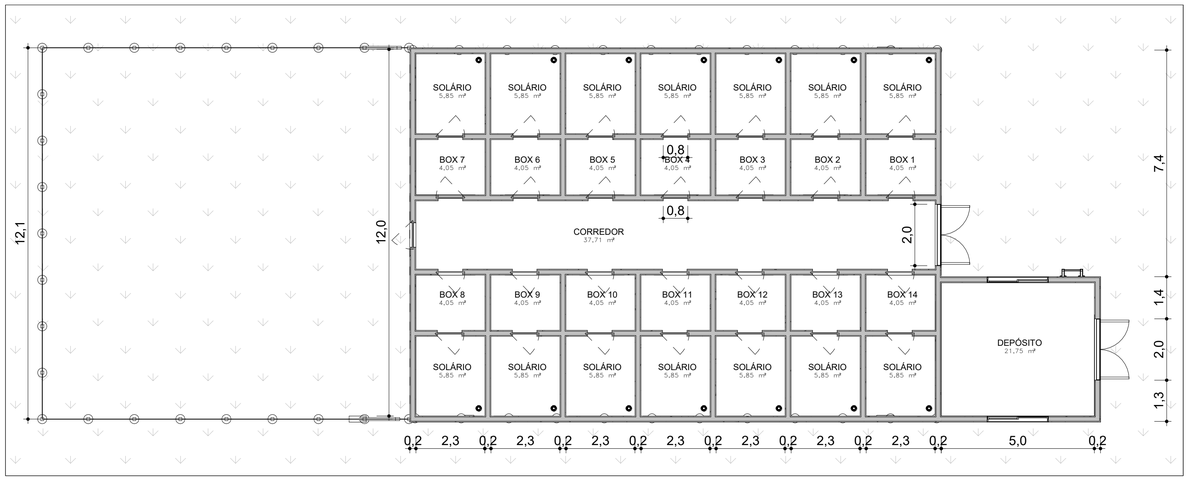



1 PLANTA TÉRREO
escala 1 : 100

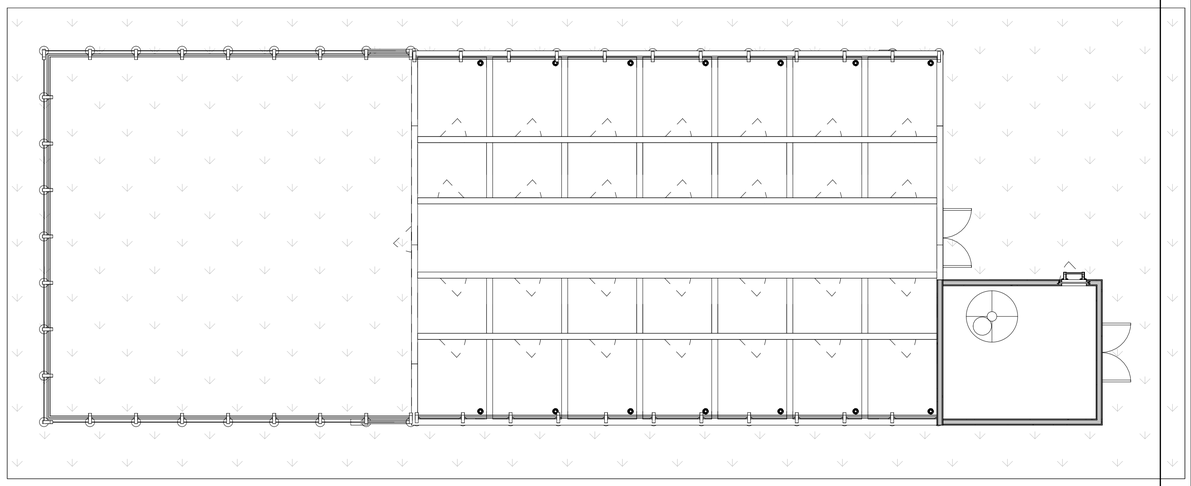

3 PLANTA LAJE
escala 1 : 100

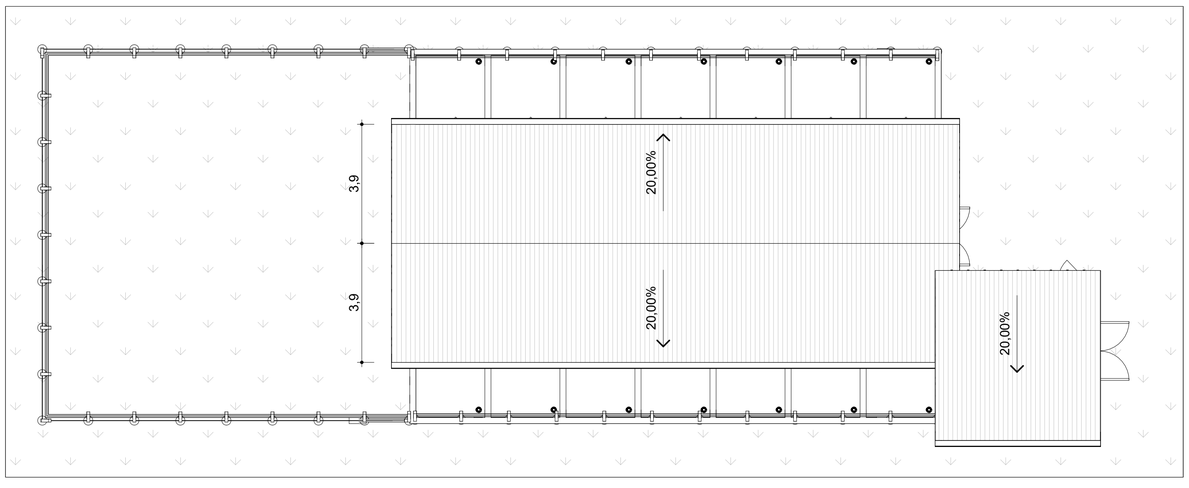

2 PLANTA TELHADO
escala 1 : 100

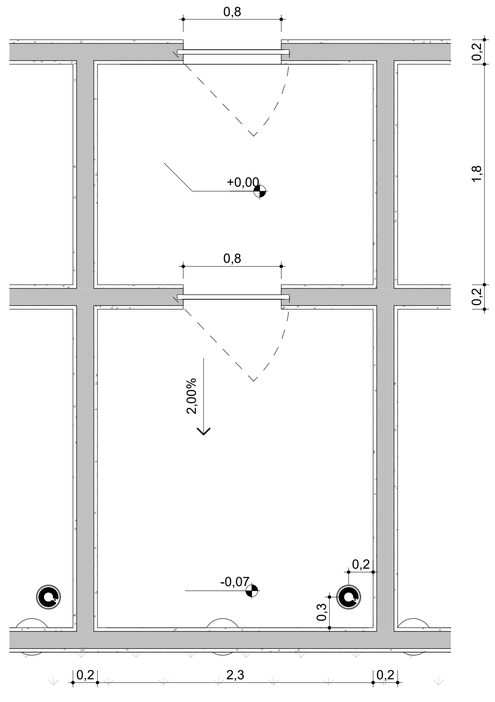

4 PLANTA BAIXA BOX TIPO
escala 1 : 25

A - TABELA JANELAS

FAMÍLIA E TIPO	LARGURA	ALTURA	PEITORIL	QUANT.
CORRER - 2 FOLHAS	2,0	1,0	1,1	2

B - TABELA DE PORTAS

FAMÍLIA E TIPO	LARGURA	ALTURA	QUANT.
PORTA DE ABRIR 02 FOLHAS COM VISOR	2,0	2,2	2
PORTÃO METÁLICO | GRADIL	0,8	<varia>	30

C - TABELA DE PISOS

FAMÍLIA E TIPO	ÁREA
Piso: NormaDOM - Osso - 15cm - Laje Concreto	21,75 m²
Piso: NormaDOM - Revestimento - 5cm - Piso Concreto	244,63 m²

D - TABELA DE PAREDES

FAMÍLIA E TIPO	COMPRIMENTO	ÁREA
Parede básica: CRO5 - Alvenaria - 20cm - Tijolo Cerâmico	199,5 m	428,49 m²

E - TABELA DE TETOS

FAMÍLIA E TIPO	ÁREA
CRO5 - Telha Fibrocimento Ondulada	175,40 m²

G - ALAMBRADO

FAMÍLIA E TIPO	COMPRIMENTO
Guarda-corpo: Alambrado	70,5 m

H - DIVERSOS

FAMÍLIA E TIPO	QUANT.
CAIXA D'ÁGUA 2000 L	1
ESCADA DE MARINHEIRO	1
RALO CIRCULAR	14

F - TABELA DE ÁREA TOTAL ÚTIL

LOCAL	ÁREA
BOX 1	4,05 m²
BOX 2	4,05 m²
BOX 3	4,05 m²
BOX 4	4,05 m²
BOX 5	4,05 m²
BOX 6	4,05 m²
BOX 7	4,05 m²
BOX 8	4,05 m²
BOX 9	4,05 m²
BOX 10	4,05 m²
BOX 11	4,05 m²
BOX 12	4,05 m²
BOX 13	4,05 m²
BOX 14	4,05 m²
CORREDOR	37,71 m²
DEPÓSITO	21,75 m²
SOLÁRIO	81,90 m²
	198,06 m²

QUADRO DE MODIFICAÇÕES

L	DATA	DESCRIÇÃO	RESP	VISTO
A				
B				
C				
D				
E				

OBSERVAÇÕES

MD EB DEC DOM	ANO	Nº OPUS	ITEM	FOLHA
IME	2026	00	AR	02/03

OM: IME	LOCAL: MARAMBAIA - BELÉM
OBRA: CONSTRUÇÃO DO CANIL DA 15º CIA PE	DATA: 11/11/26
PRANCHA: CONSOLIDACAO - PLANTA GERAL E QUANTITATIVOS	DIM: METRO
AUTOR: CAP FELIPE MIRANDA / VISTO AUTOR	DESENHISTA: Autor
CH SEC TEC / VISTO CH SEC TEC	ESCALA: INDICADA
CH CRO 5 / VISTO CH CRO	ARQUIVO: arquivo.rvt

Rua 31 De Março,3016 – Pinheirinho, Curitiba–PR
Cep: 81110-260 / Fone:(41) 3366-0147