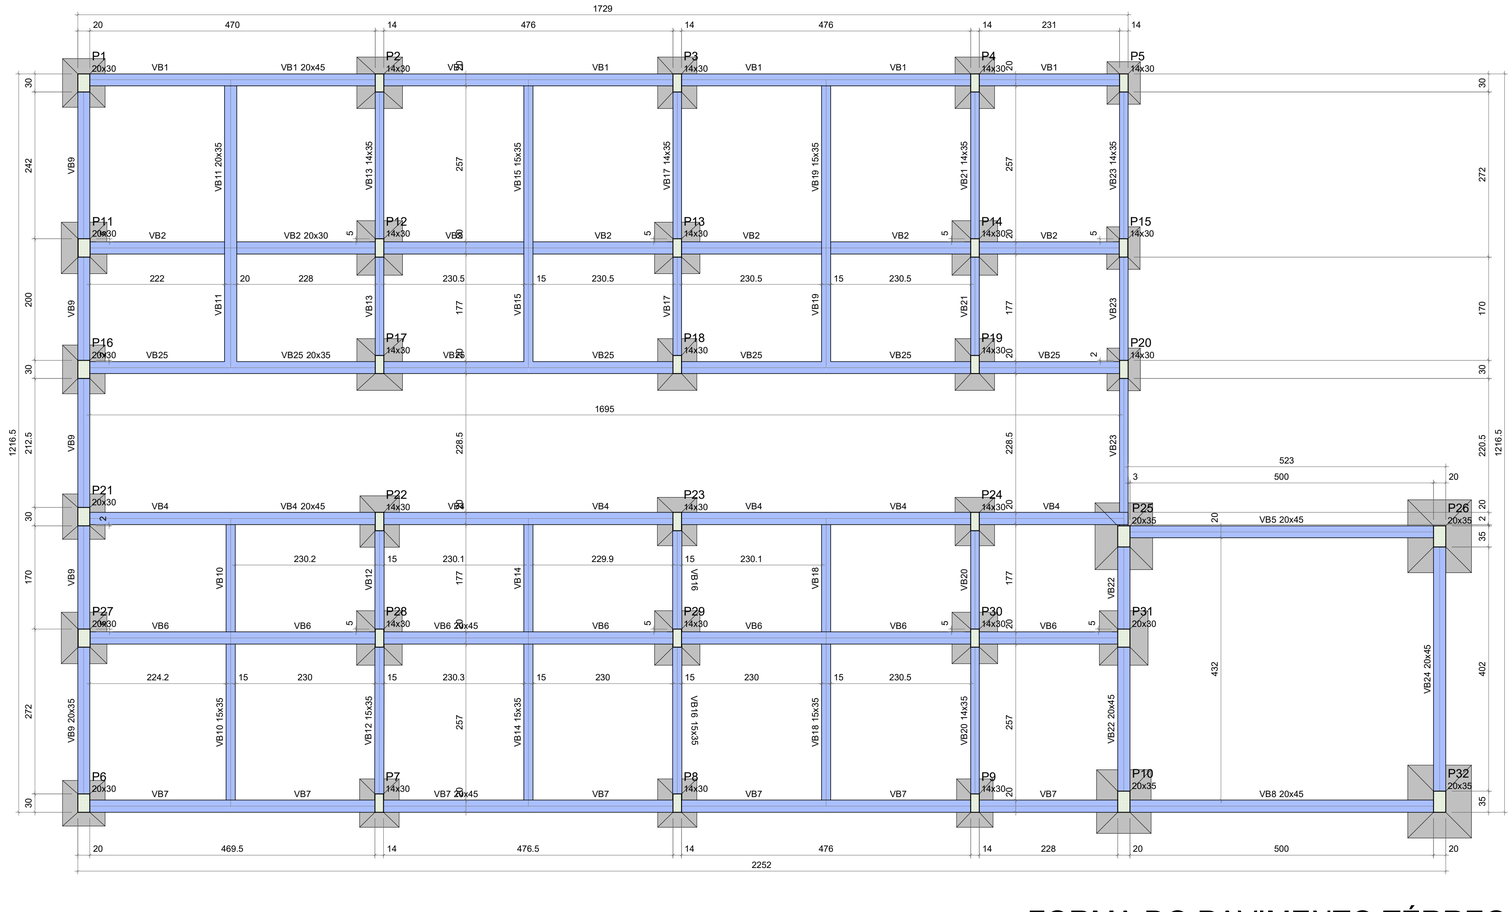


FORMA DO PAVIMENTO TÉRREO

Escala 1:50

Vigas			
Nome	Seção (cm)	Elevação (cm)	Nível (cm)
VB1	20x45	0	0
VB2	20x30	0	0
VB4	20x45	0	0
VB5	20x45	0	0
VB6	20x45	0	0
VB7	20x45	0	0
VB8	20x45	0	0
VB9	20x35	0	0
VB10	15x35	0	0
VB11	20x35	0	0
VB12	15x35	0	0
VB13	14x35	0	0
VB14	15x35	0	0
VB15	15x35	0	0
VB16	15x35	0	0
VB17	14x35	0	0
VB18	15x35	0	0
VB19	15x35	0	0
VB20	14x35	0	0
VB21	14x35	0	0
VB22	20x45	0	0
VB23	14x35	0	0
VB24	20x45	0	0
VB25	20x35	0	0

Características dos materiais

fck (MPa)	Ecs (MPa)
25	24150

Dimensão máxima do agregado = 19 mm

Pilares			
Nome	Seção (cm)	Elevação (cm)	Nível (cm)
P1	20x30	0	0
P2	14x30	0	0
P3	14x30	0	0
P4	14x30	0	0
P5	14x30	0	0
P6	20x30	0	0
P7	14x30	0	0
P8	14x30	0	0
P9	14x30	0	0
P10	20x35	0	0
P11	20x30	0	0
P12	14x30	0	0
P13	14x30	0	0
P14	14x30	0	0
P15	14x30	0	0
P16	20x30	0	0
P17	14x30	0	0
P18	14x30	0	0
P19	14x30	0	0
P20	14x30	0	0
P21	20x30	0	0
P22	14x30	0	0
P23	14x30	0	0
P24	14x30	0	0
P25	20x35	0	0
P26	20x35	0	0
P27	20x30	0	0
P28	14x30	0	0
P29	14x30	0	0
P30	14x30	0	0
P31	20x30	0	0
P32	20x35	0	0

Legenda dos pilares
Pilar que passa

Legenda das vigas e paredes
Viga

CAP FELIPE MIRANDA - IME