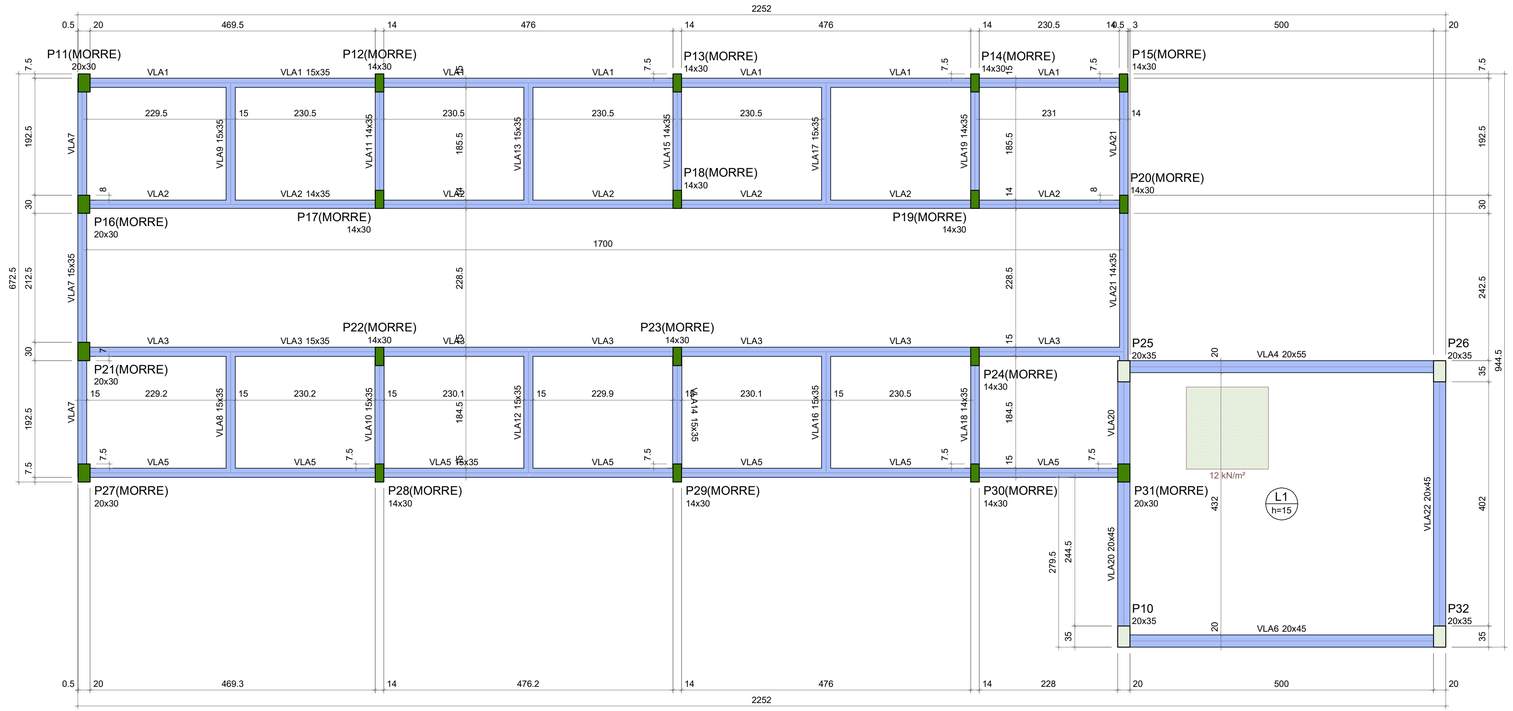


FORMA DO PAVIMENTO TELHADO CANIL E LAJE DEPOSITO

Escala 1:50

Vigas			
Nome	Seção (cm)	Elevação (cm)	Nível (cm)
VLA1	15x35	0	300
VLA2	14x35	0	300
VLA3	15x35	0	300
VLA4	20x55	0	300
VLA5	15x35	0	300
VLA6	20x45	0	300
VLA7	15x35	0	300
VLA8	15x35	0	300
VLA9	15x35	0	300
VLA10	15x35	0	300
VLA11	14x35	0	300
VLA12	15x35	0	300
VLA13	15x35	0	300
VLA14	15x35	0	300
VLA15	14x35	0	300
VLA16	15x35	0	300
VLA17	15x35	0	300
VLA18	14x35	0	300
VLA19	14x35	0	300
VLA20	20x45	0	300
VLA21	14x35	0	300
VLA22	20x45	0	300

Lajes								
		Dados				Sobrecarga (kN/m²)		
Nome	Tipo	Altura (cm)	Elevação (cm)	Nível (cm)	Peso próprio (kN/m²)	Adicional	Acidental	Localizada
L1	Maciça	15	0	300	3.75	1.37	1.50	sim

Características dos materiais

fck (MPa)	Ecs (MPa)
25	24150

Dimensão máxima do agregado = 19 mm

Pilares			
Nome	Seção (cm)	Elevação (cm)	Nível (cm)
P10	20x35	0	300
P11	20x30	0	300
P12	14x30	0	300
P13	14x30	0	300
P14	14x30	0	300
P15	14x30	0	300
P16	20x30	0	300
P17	14x30	0	300
P18	14x30	0	300
P19	14x30	0	300
P20	14x30	0	300
P21	20x30	0	300
P22	14x30	0	300
P23	14x30	0	300
P24	14x30	0	300
P25	20x35	0	300
P26	20x35	0	300
P27	20x30	0	300
P28	14x30	0	300
P29	14x30	0	300
P30	14x30	0	300
P31	20x30	0	300
P32	20x35	0	300

Legenda dos pilares
Pilar que morre
Pilar que passa

Legenda das vigas e paredes
Viga